

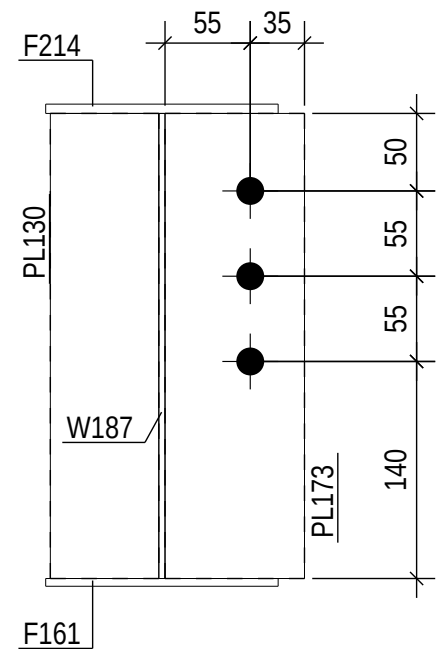
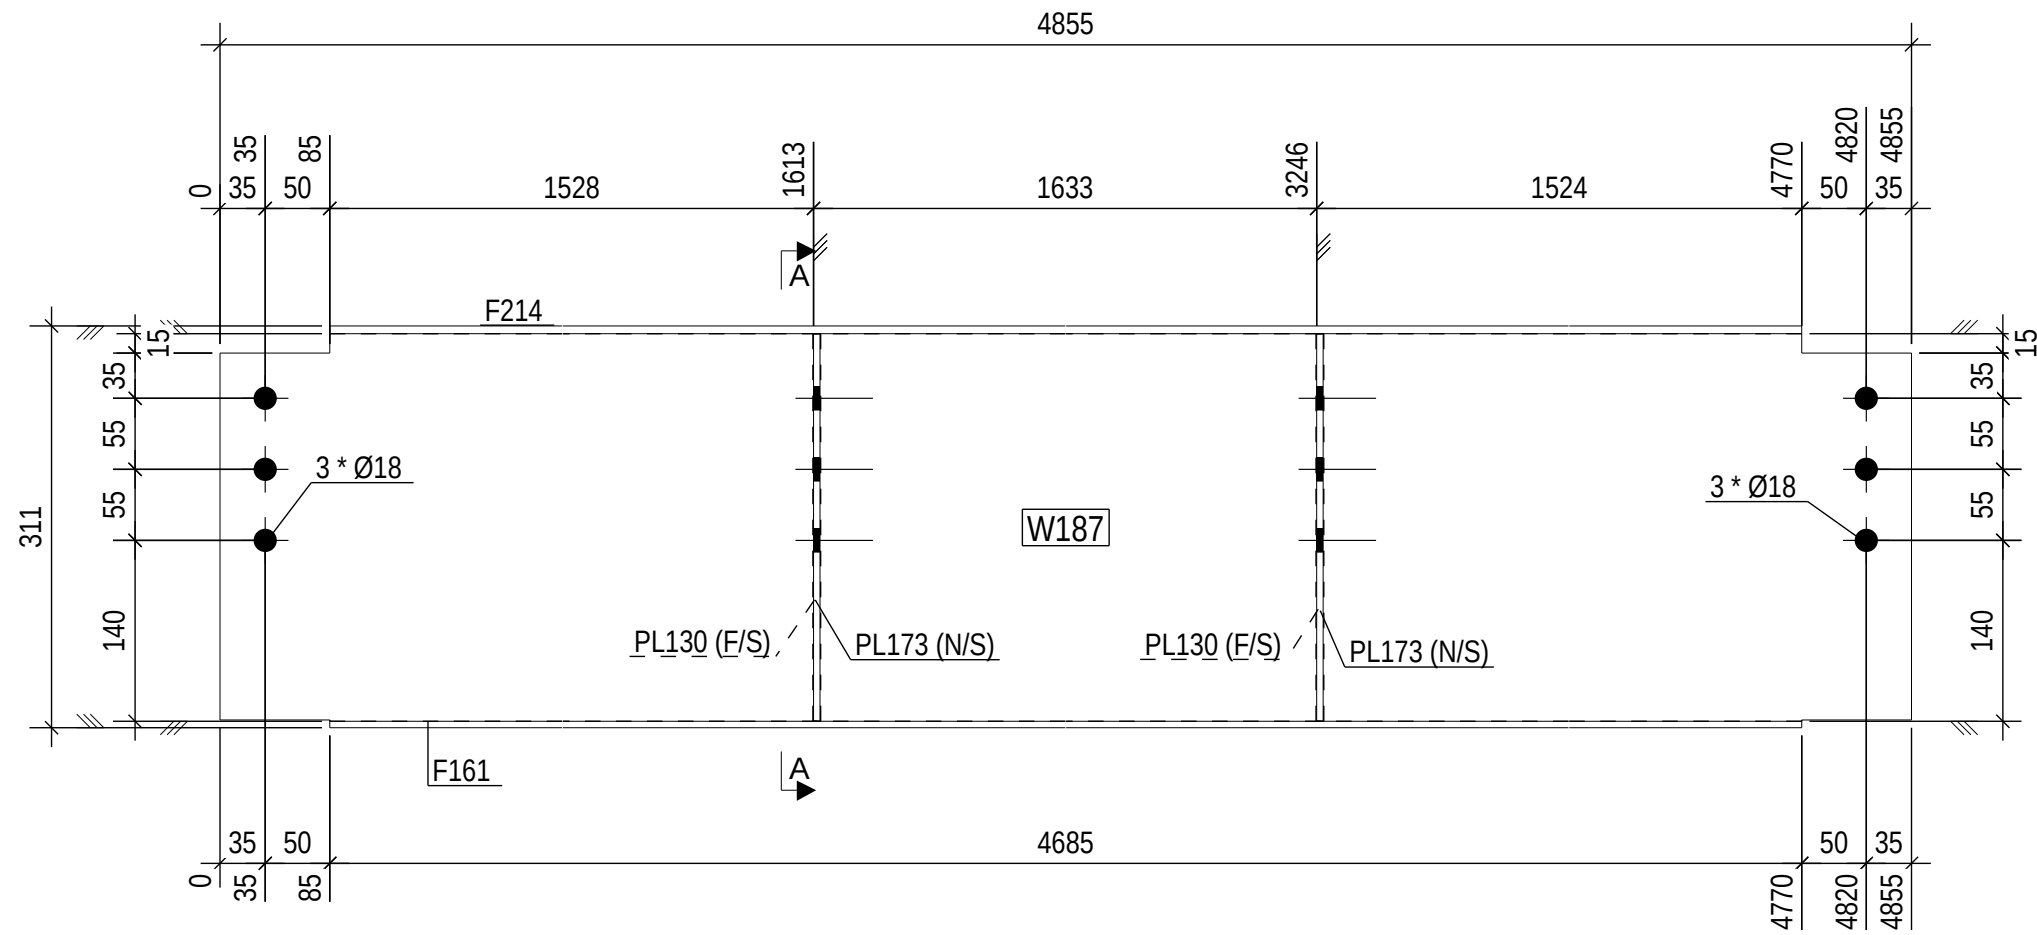


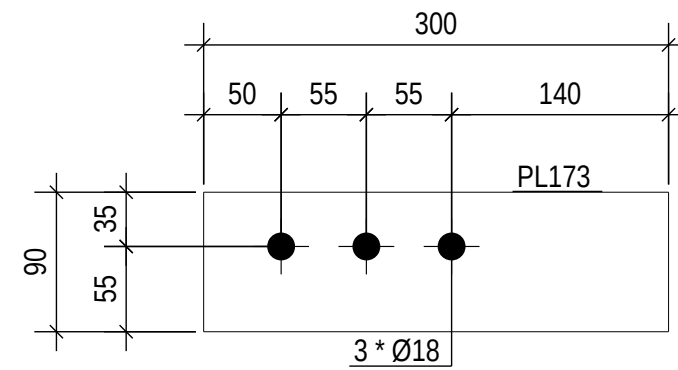

SEC A
1:5

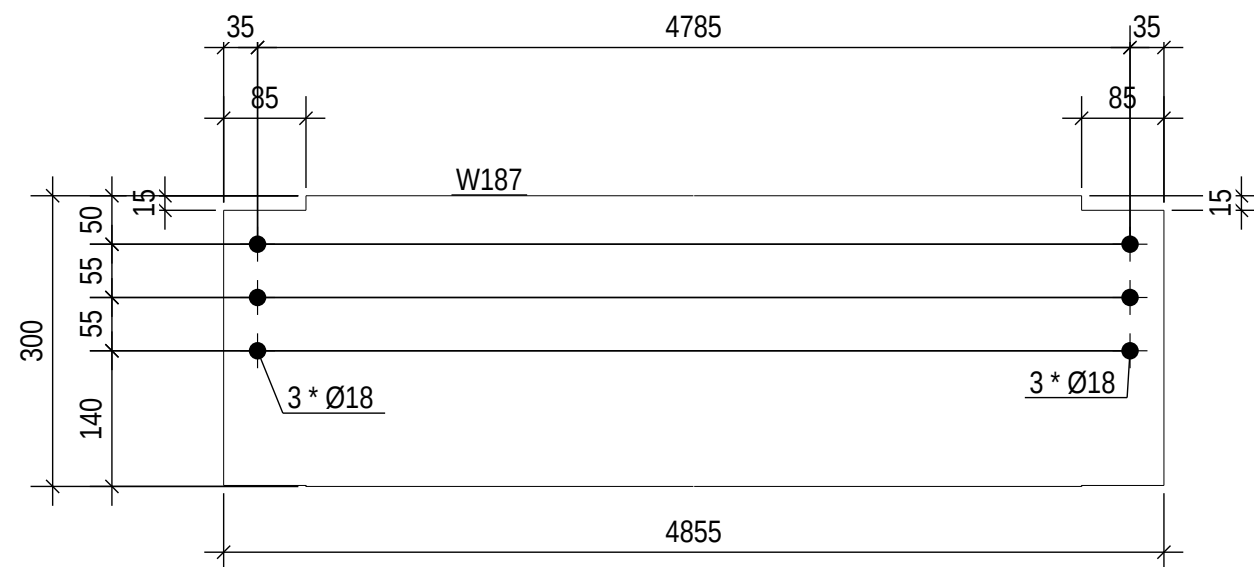

QTY= 2 Nos. MEZZ. JOIST MKD : MJ26

00	23.10.2025	ISSUED FOR FABRICATION	SF	MMN	AMA
REV.	DATE	DESCRIPTION	DRW	CHK	APP
SBN015-2025					
DRAWN	SF		DATE	23.10.2025	
CHECKED	MMN		SCALE	1:5	
REVIEWED	AMA		REL. NO.	REL02	
ASSEMBLY MARK			SHT. NO.	REV. NO.	
MJ26				00	