


Tekla structures

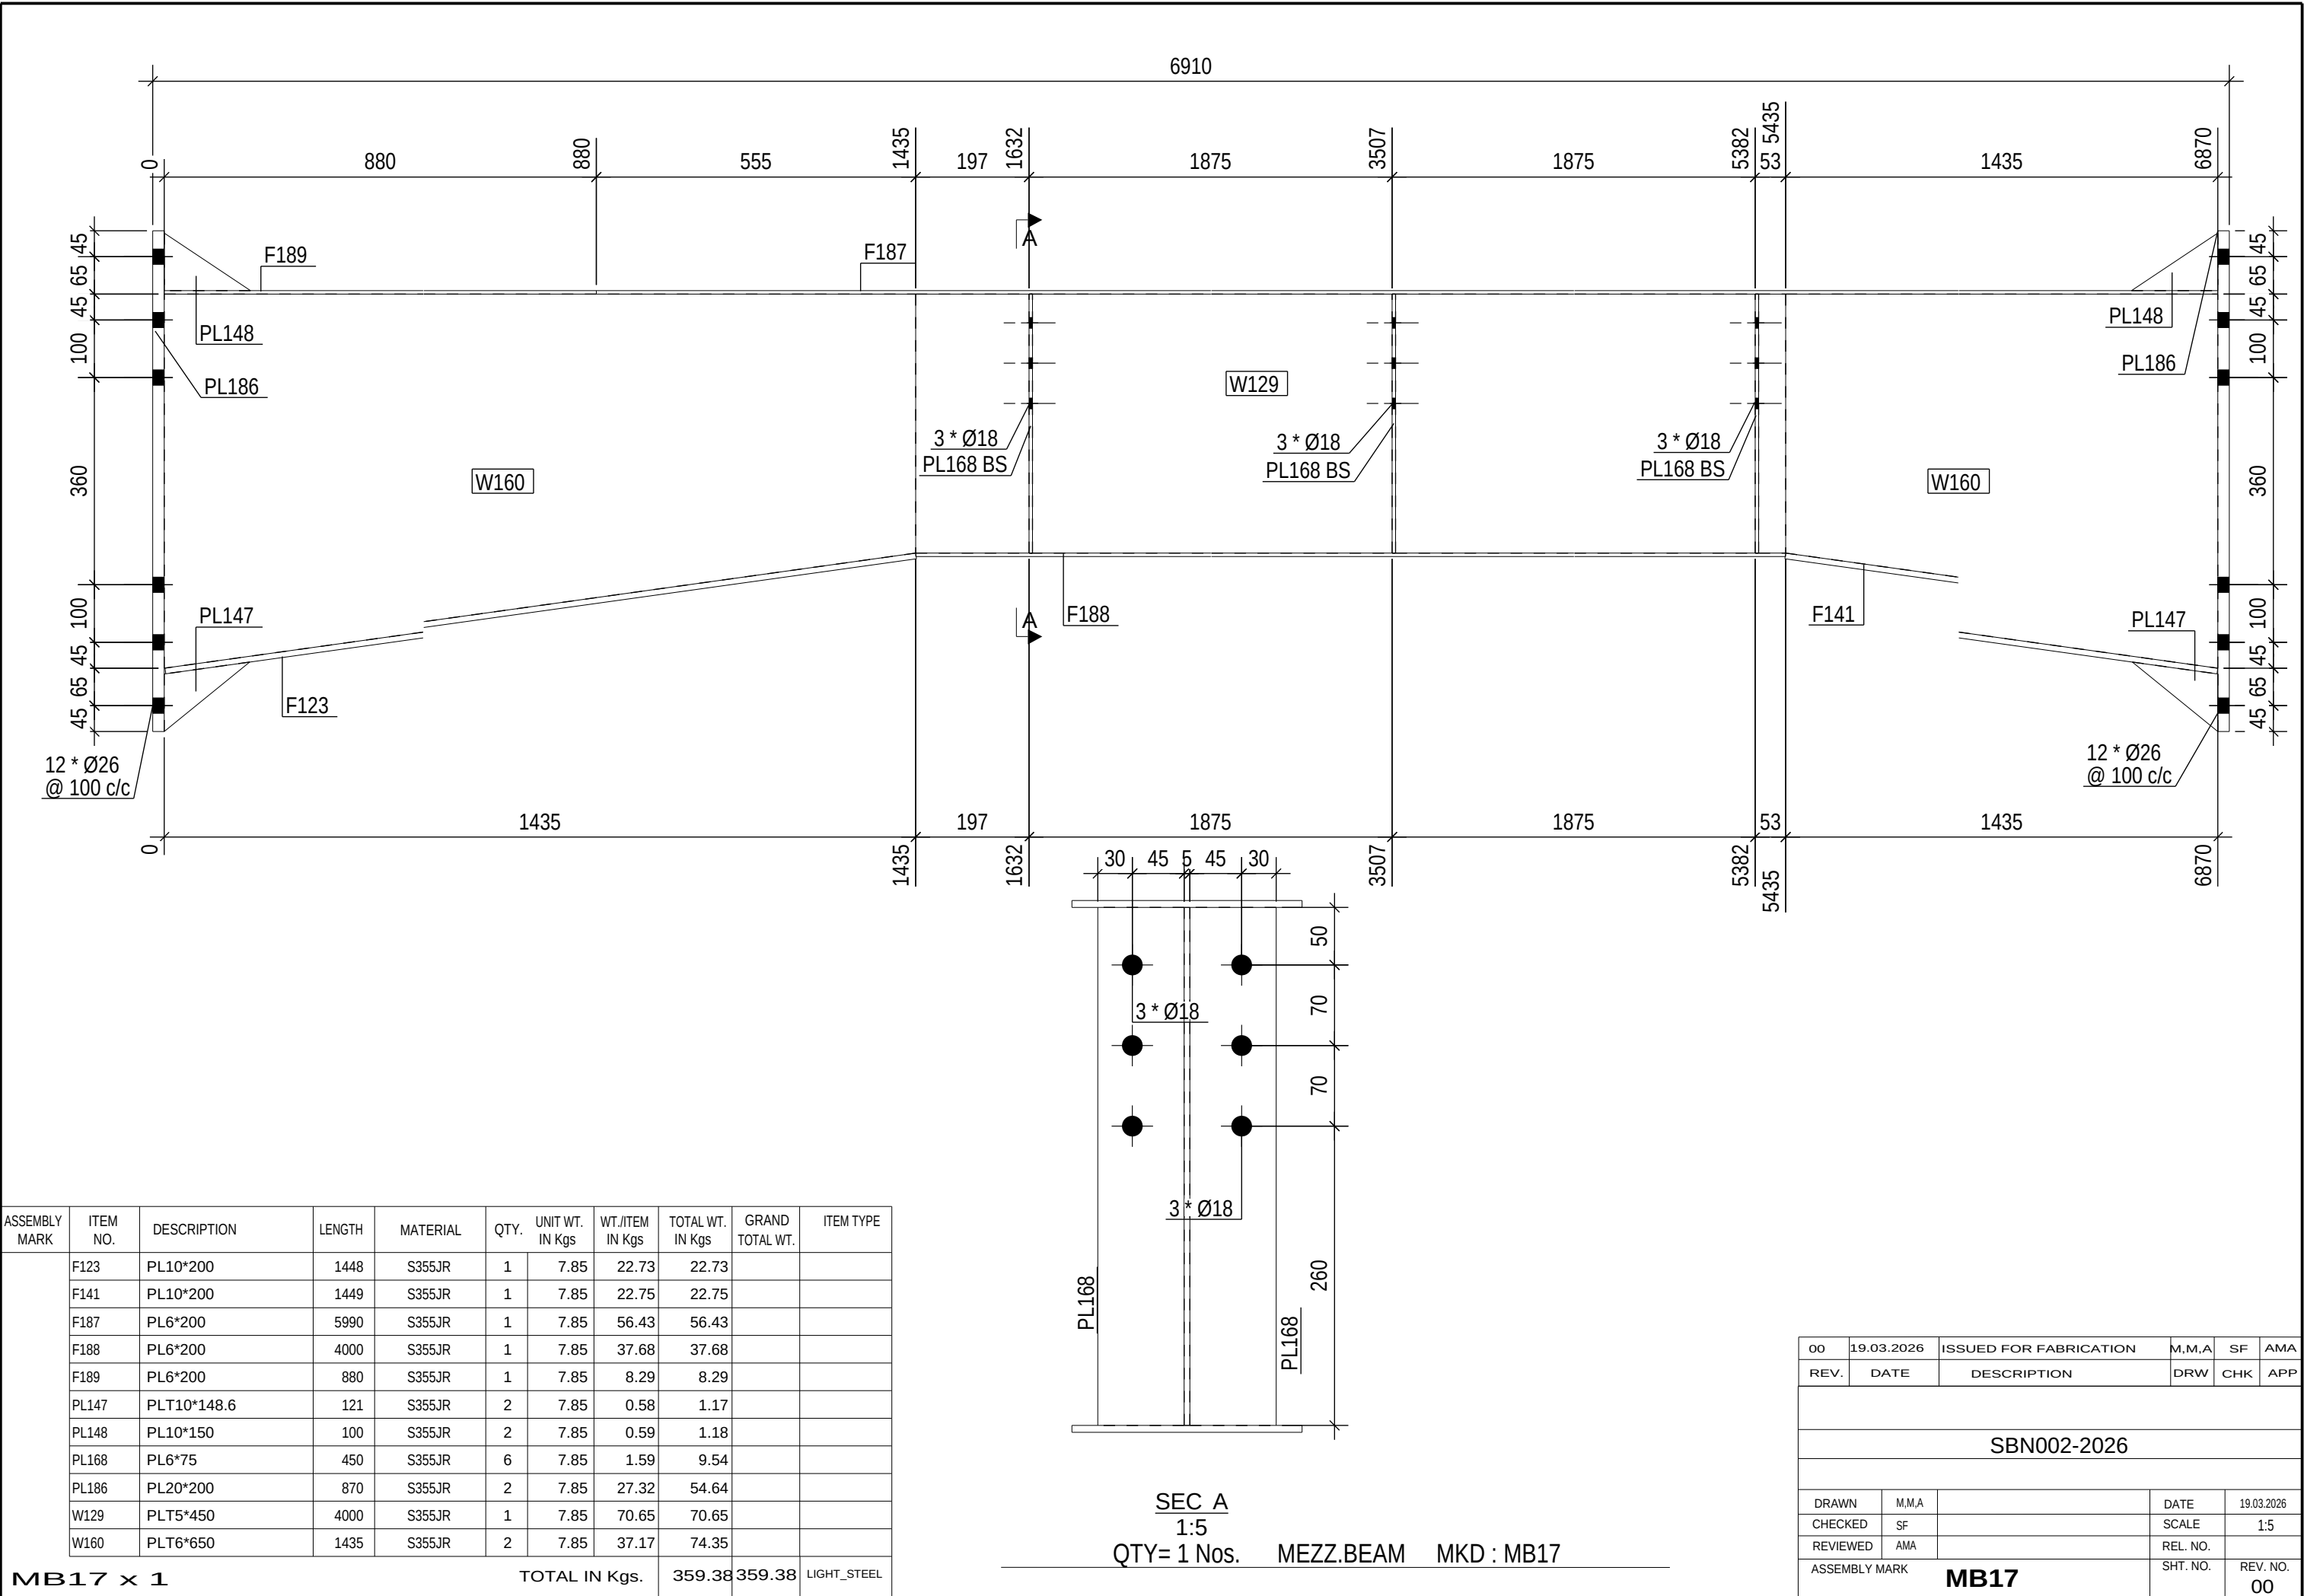

MB17 x 1

SEC A
1:5
QTY= 1 Nos. MEZZ.BEAM MKD : MB17