


Taka Structures

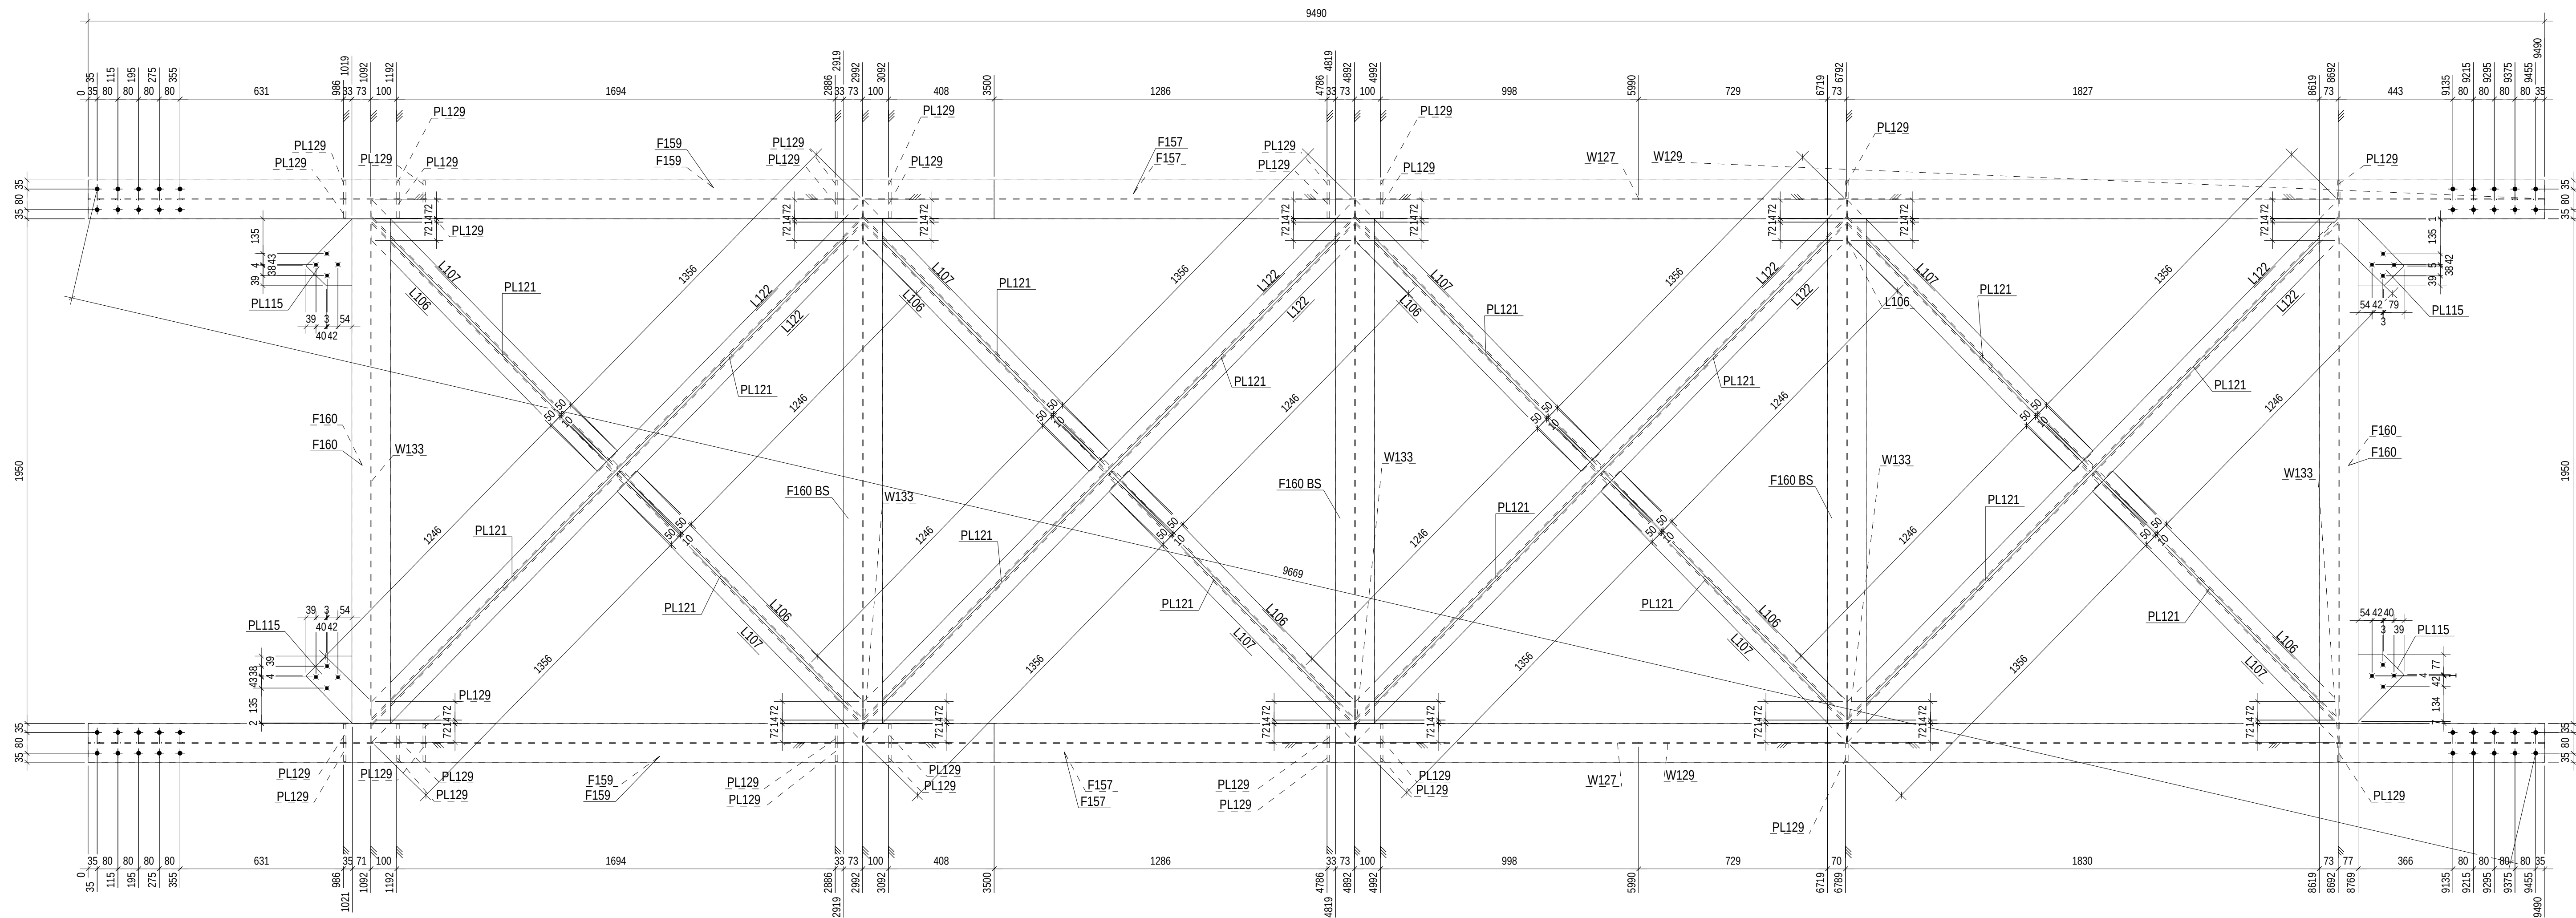

QTY= 1 Nos. TRUSS MKD : TR3

00	29.01.2026	ISSUED FOR FABRICATION	SF&MM	AMA	AMA
REV.	DATE	DESCRIPTION	DRW	CHK	APP
SPN073-2025					
DRAWN	SF&MM		DATE	29.01.2026	
CHECKED	AMA		SCALE	1:13	
REVIEWED	AMA		REL. NO.	REL02	
ASSEMBLY MARK	TR3		SRT. NO.	REV. NO. 00	