


Tekla structures

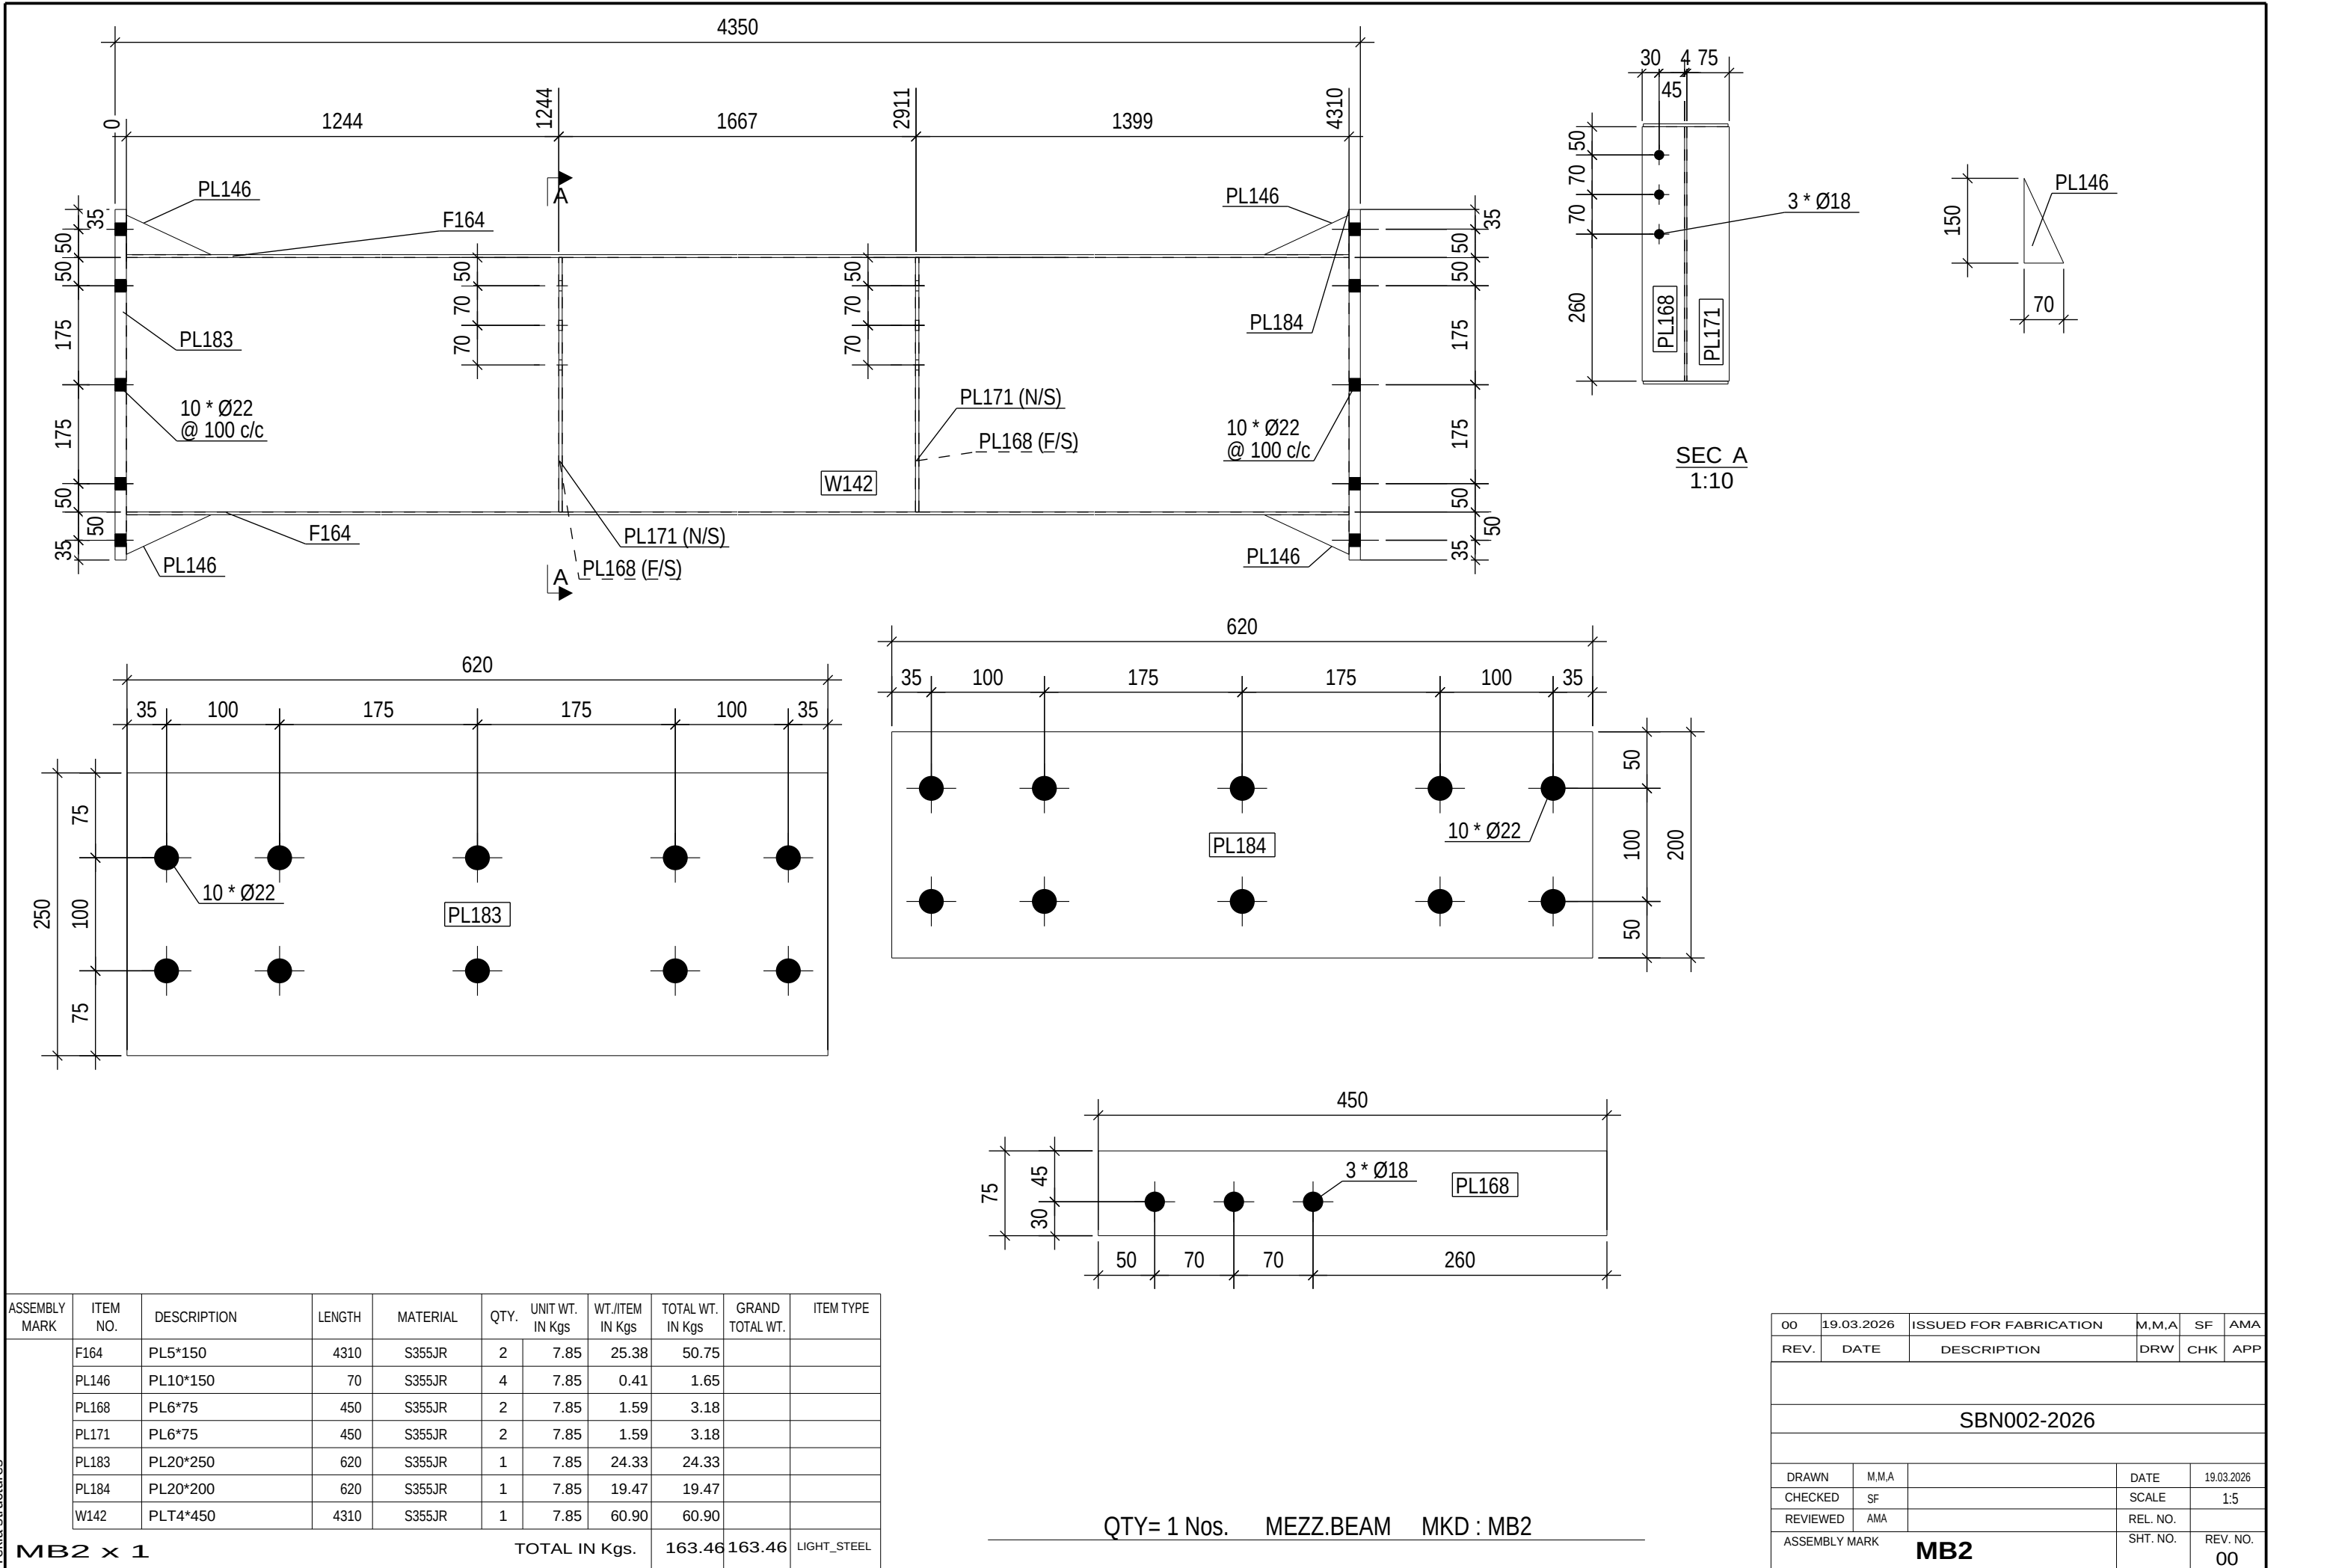

00	19.03.2026	ISSUED FOR FABRICATION	M,M,A	SF	AMA
REV.	DATE	DESCRIPTION	DRW	CHK	APP
SBN002-2026					
DRAWN	M,M,A		DATE	19.03.2026	
CHECKED	SF		SCALE	1:5	
REVIEWED	AMA		REL. NO.		
ASSEMBLY MARK			SHT. NO.	REV. NO.	
MB2				00	