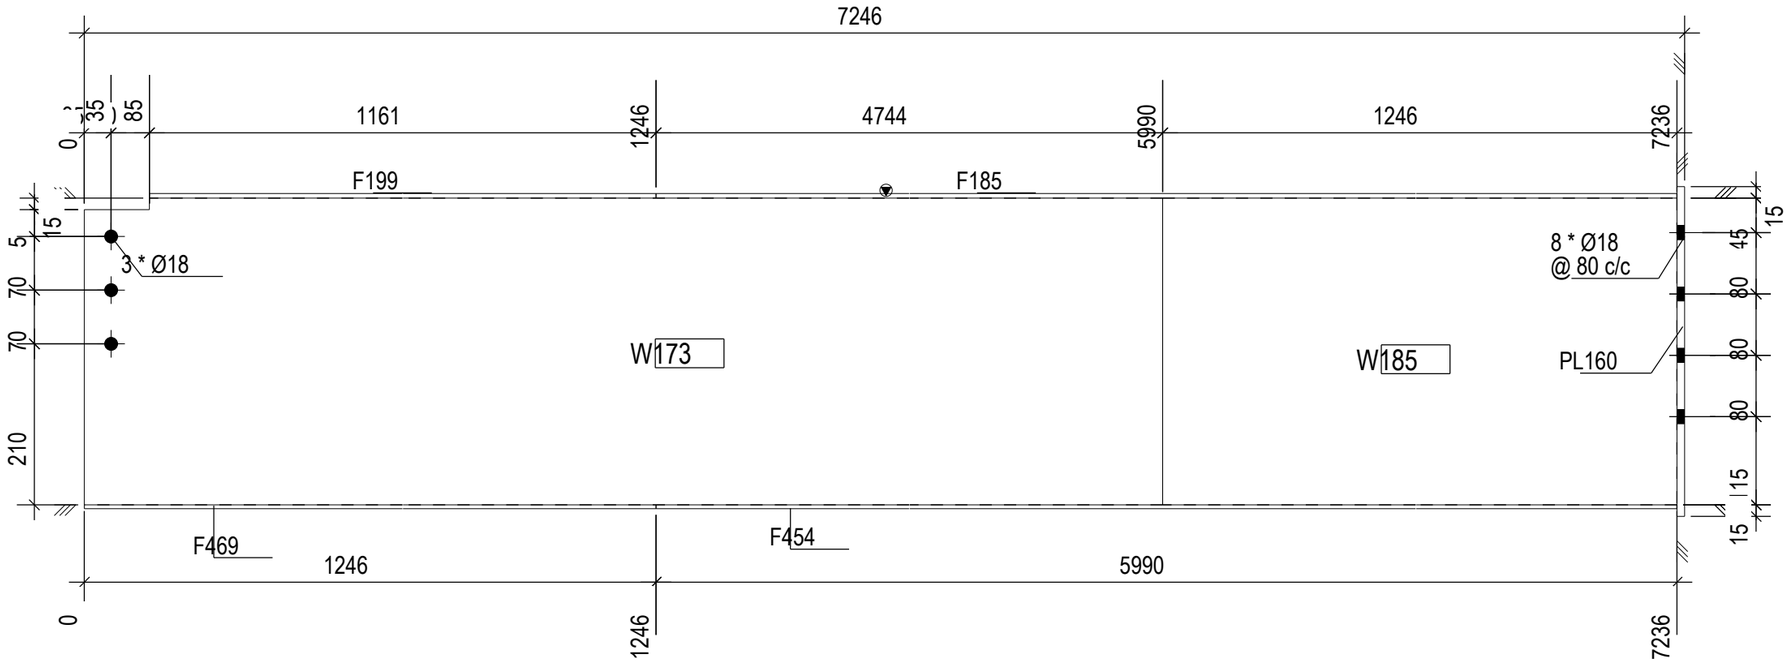

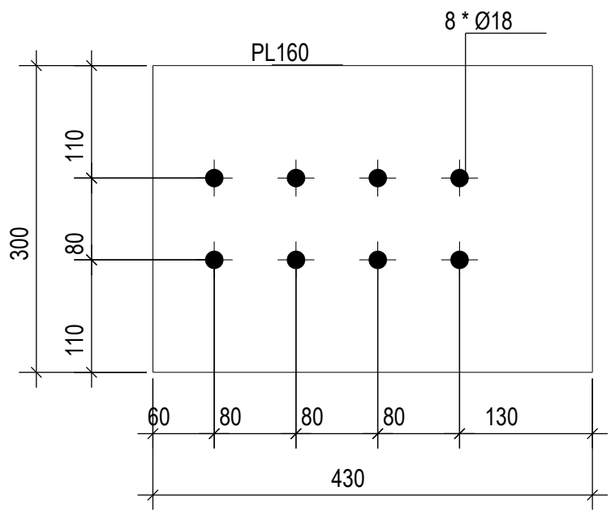

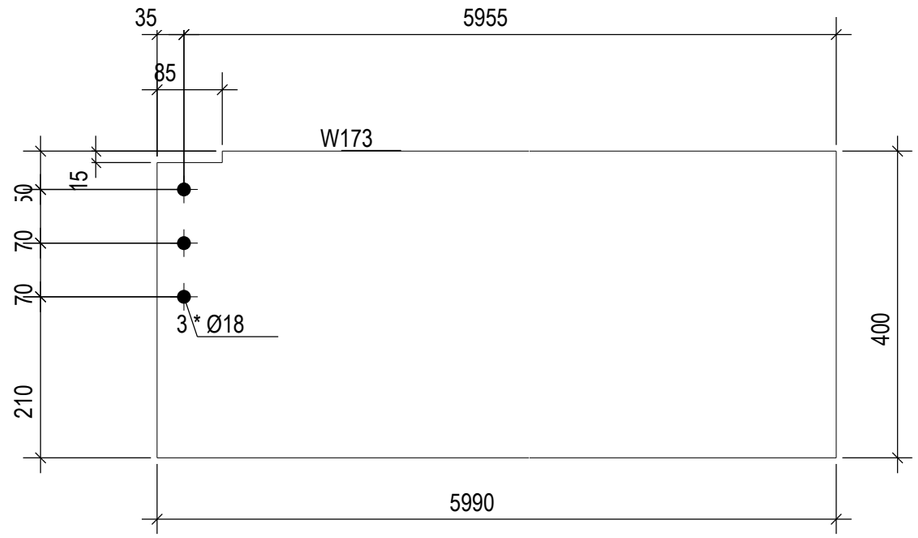

QTY= 2 Nos. JOIST MKD : MJ28

Tekla structures