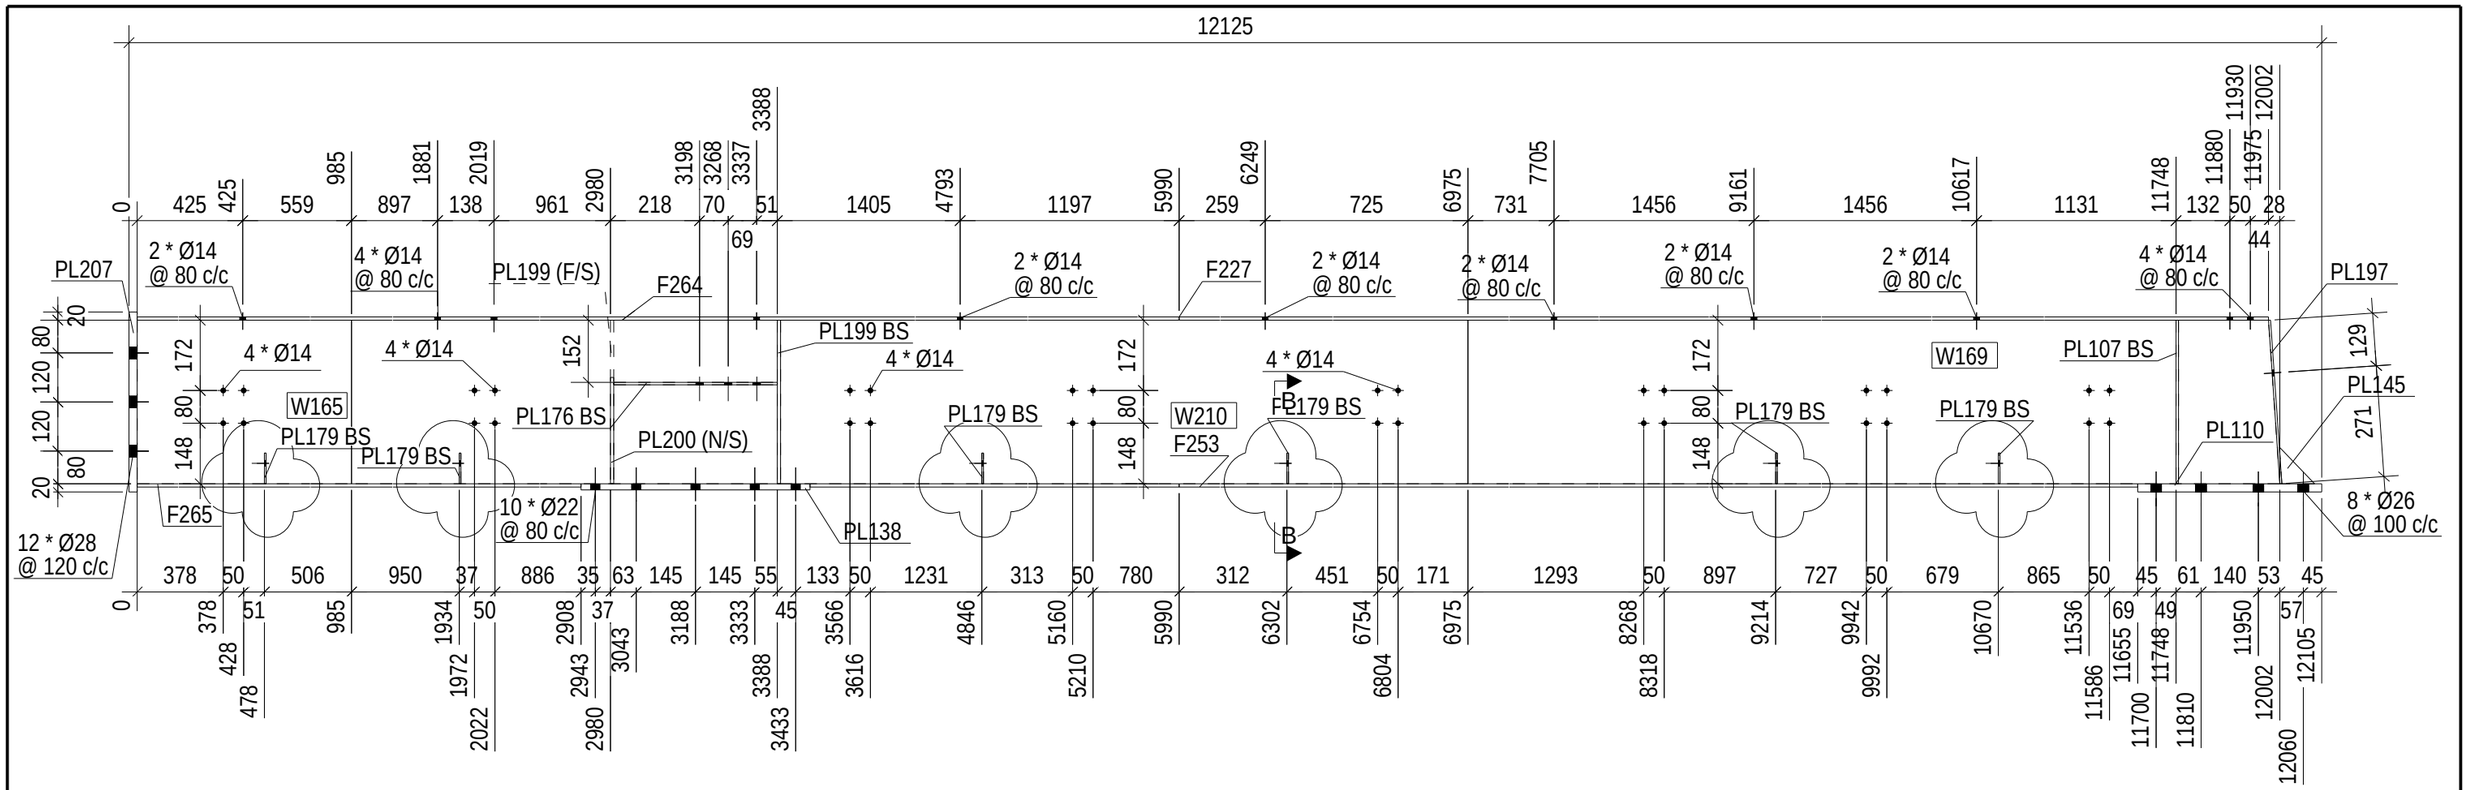

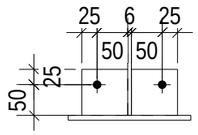

SEC B
1:10

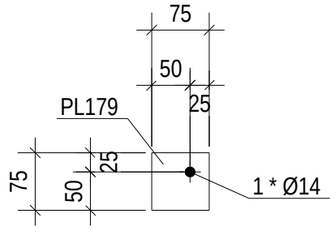

REV01
ADD 12X PL179

ASSEMBLY MARK	ITEM NO.	DESCRIPTION	LENGTH	MATERIAL	QTY.	UNIT WT. IN Kgs	WT./ITEM IN Kgs	TOTAL WT. IN Kgs	GRAND TOTAL WT.	ITEM TYPE
	F227	PL8*200	5985	S355JR	1	7.85	75.17	75.17		
	F253	PL8*200	5665	S355JR	1	7.85	71.15	71.15		
	F264	PL8*200	5990	S355JR	1	7.85	75.23	75.23		
	F265	PL8*200	5990	S355JR	1	7.85	68.20	68.20		
	PL107	PL6*90	400	S355JR	2	7.85	1.70	3.39		
	PL110	PL20*200	450	S355JR	1	7.85	14.13	14.13		
	PL138	PL15*200	560	S355JR	1	7.85	13.19	13.19		
	PL145	PLT10*86.2	90	S355JR	1	7.85	0.28	0.28		
	PL176	PL6*80	400	S355JR	1	7.85	1.51	1.51		
	PL179	PLT4*75	75	S355JR	12	7.85	0.18	2.12		
	PL193	PL6*80	400	S355JR	1	7.85	1.51	1.51		
	PL197	PLT5*200	401	S355JR	1	7.85	3.14	3.14		
	PL199	PL8*90	400	S355JR	3	7.85	2.26	6.78		
	PL200	PL8*90	260	S355JR	1	7.85	1.47	1.47		
	PL207	PL20*220	440	S355JR	1	7.85	15.20	15.20		
	W165	PLT6*400	985	S355JR	1	7.85	18.55	18.55		
	W169	PLT6*400	5028	S355JR	1	7.85	94.46	94.46		
	W210	PLT6*400	5990	S355JR	1	7.85	112.85	112.85		
EWC9 x 1						TOTAL IN Kgs.		578.33	578.33	LIGHT_STEEL

QTY= 1 Nos. END WALL COLUMN MKD : EWC9

REV.	DATE	DESCRIPTION	DRW	CHK	APP
01	29.03.2026	ISSUED FOR FABRICATION	M A A	SF	MAB
00	28.03.2026	ISSUED FOR FABRICATION	AZ	SF	AMA

SBN022-2024

DRAWN	M A A		DATE	29.03.2026
CHECKED	SF		SCALE	1:5
REVIEWED	MAB		REL. NO.	REL03
ASSEMBLY MARK	EWC9		SHT. NO.	REV. NO. 01

Tekla structures