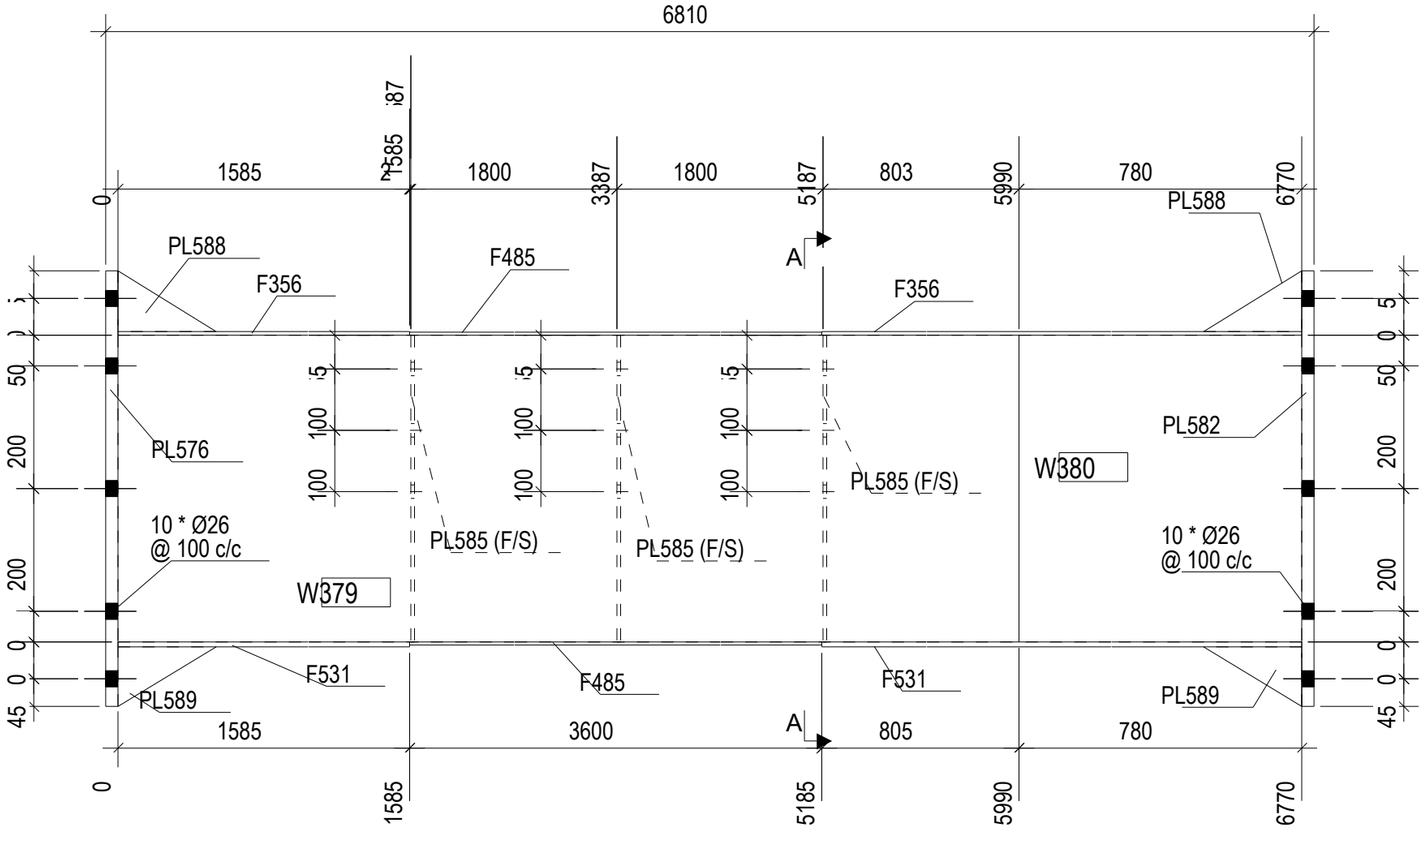

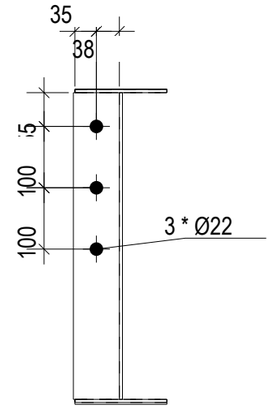

SEC A
1:10

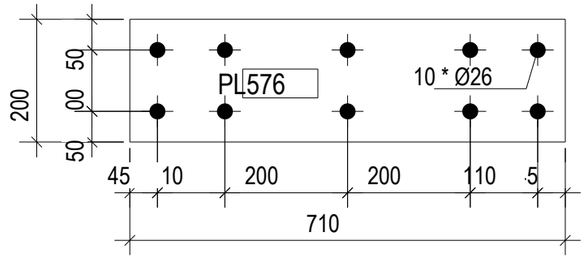

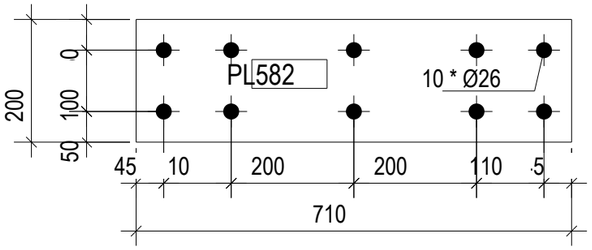

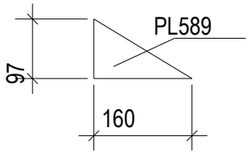

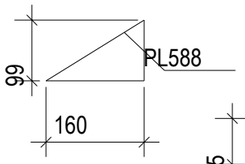

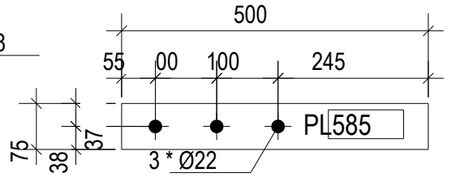

QTY= 1 Nos. MEZZ.BEAM MKD : MB502