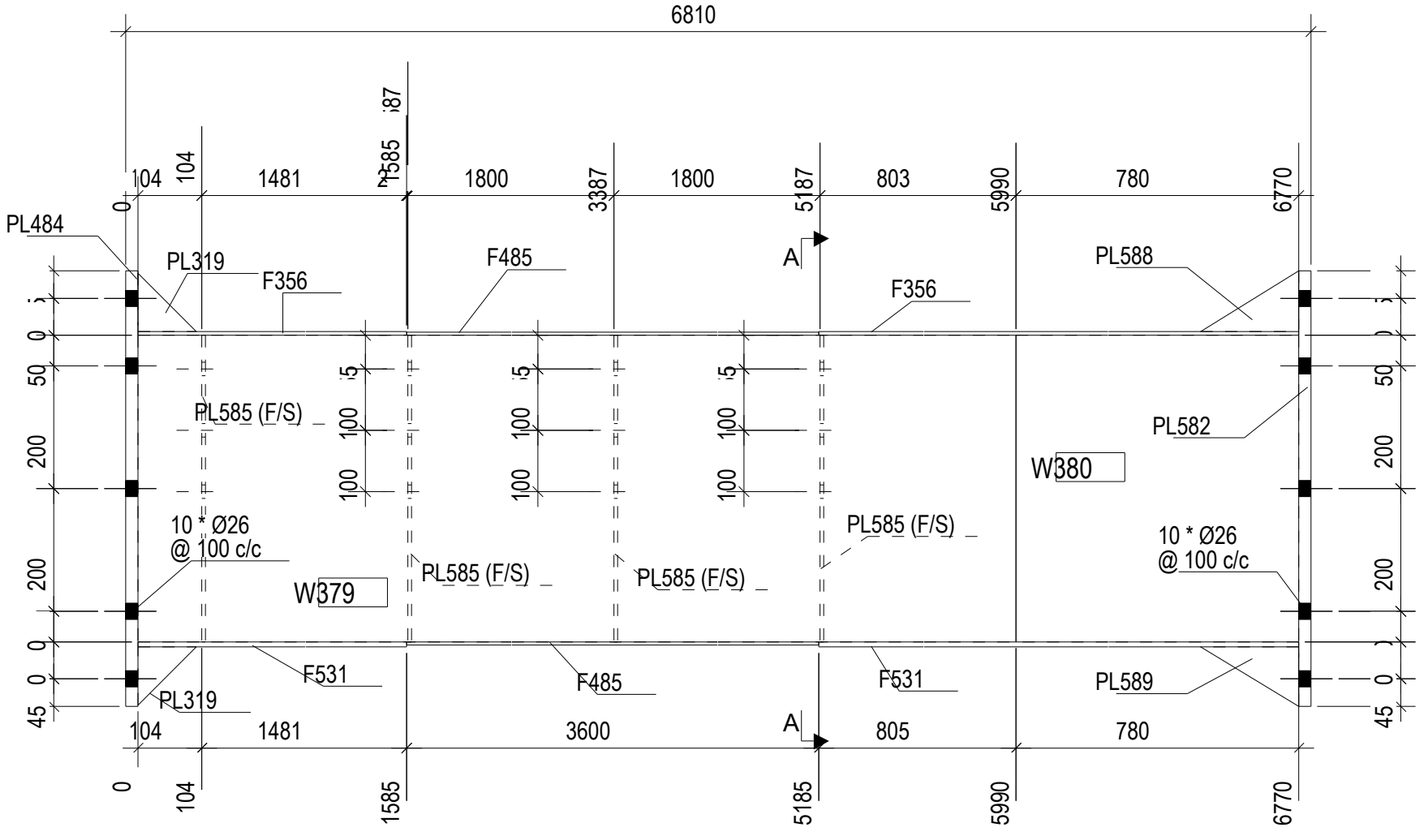

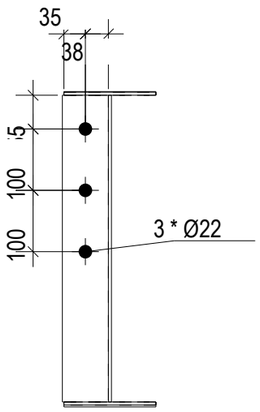

SEC A
1:10

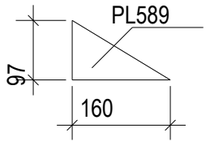

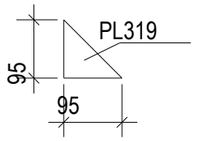

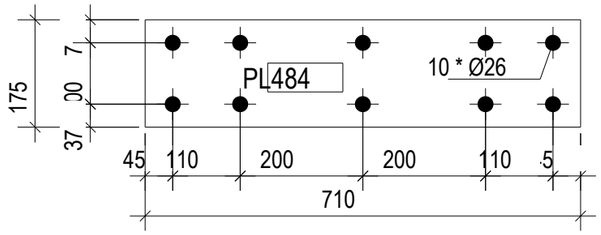

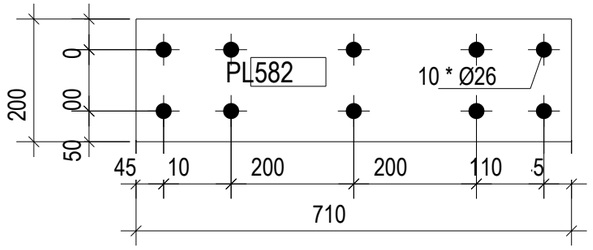

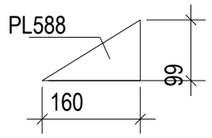

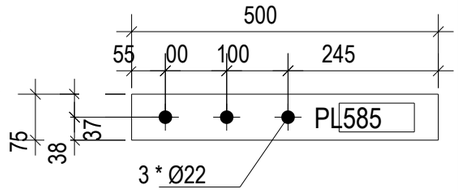

QTY= 1 Nos. MEZZ.BEAM MKD : MB503

Tekla structures