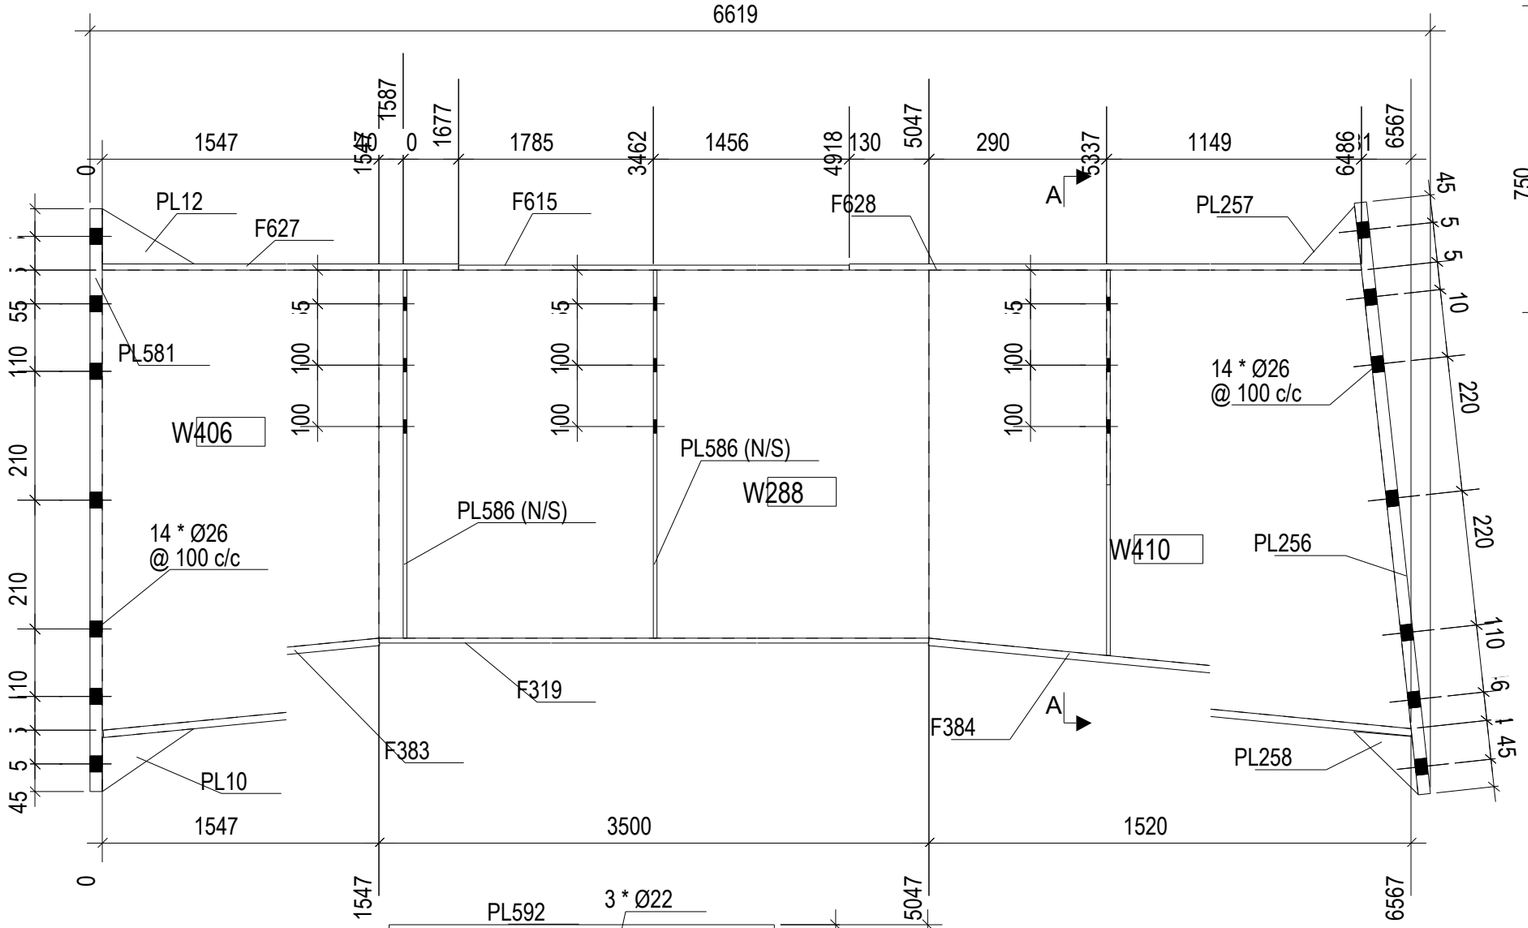

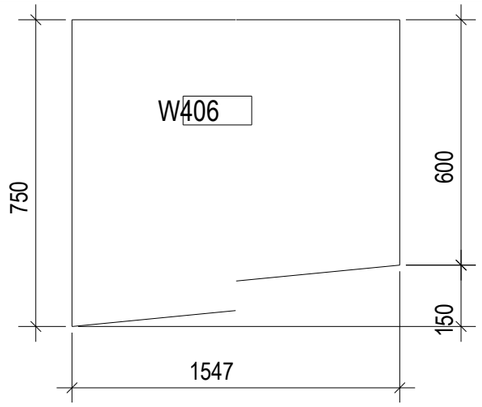

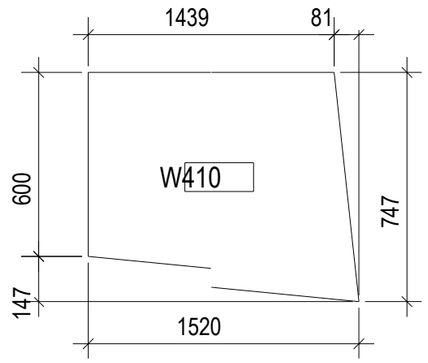

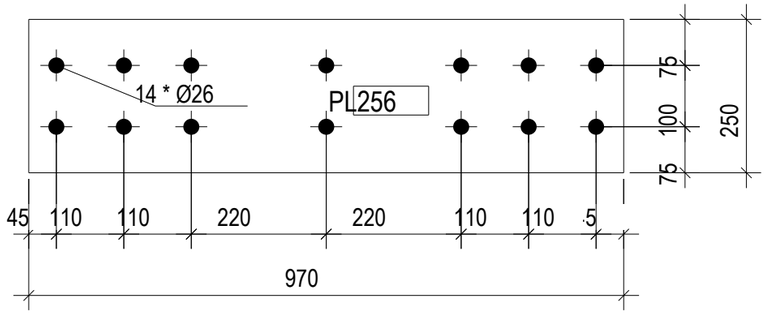

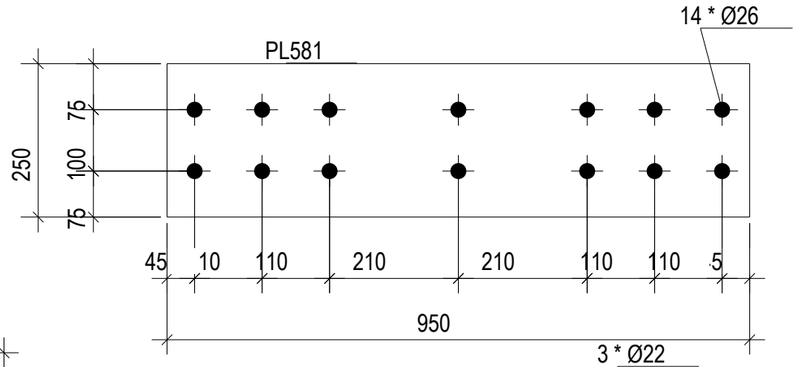

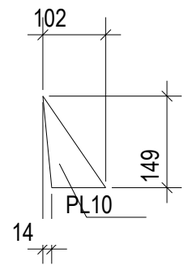

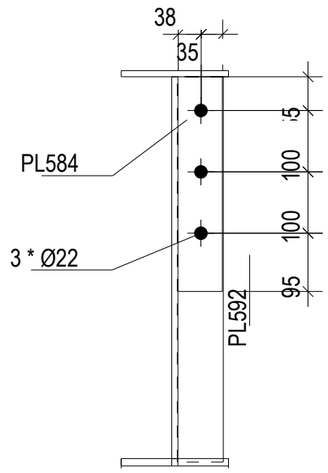

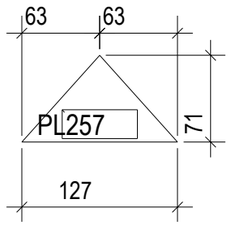

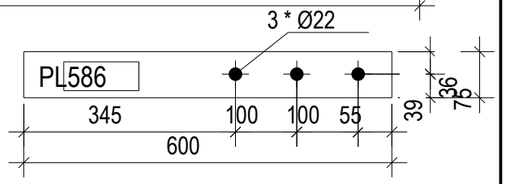

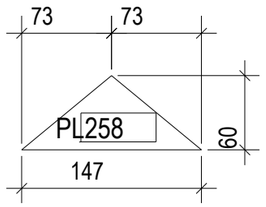

SEC A
1:10

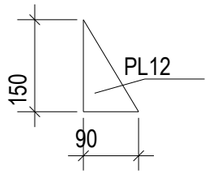

QTY= 1 Nos. MEZZ.BEAM MKD : MB504

Tekla structures